


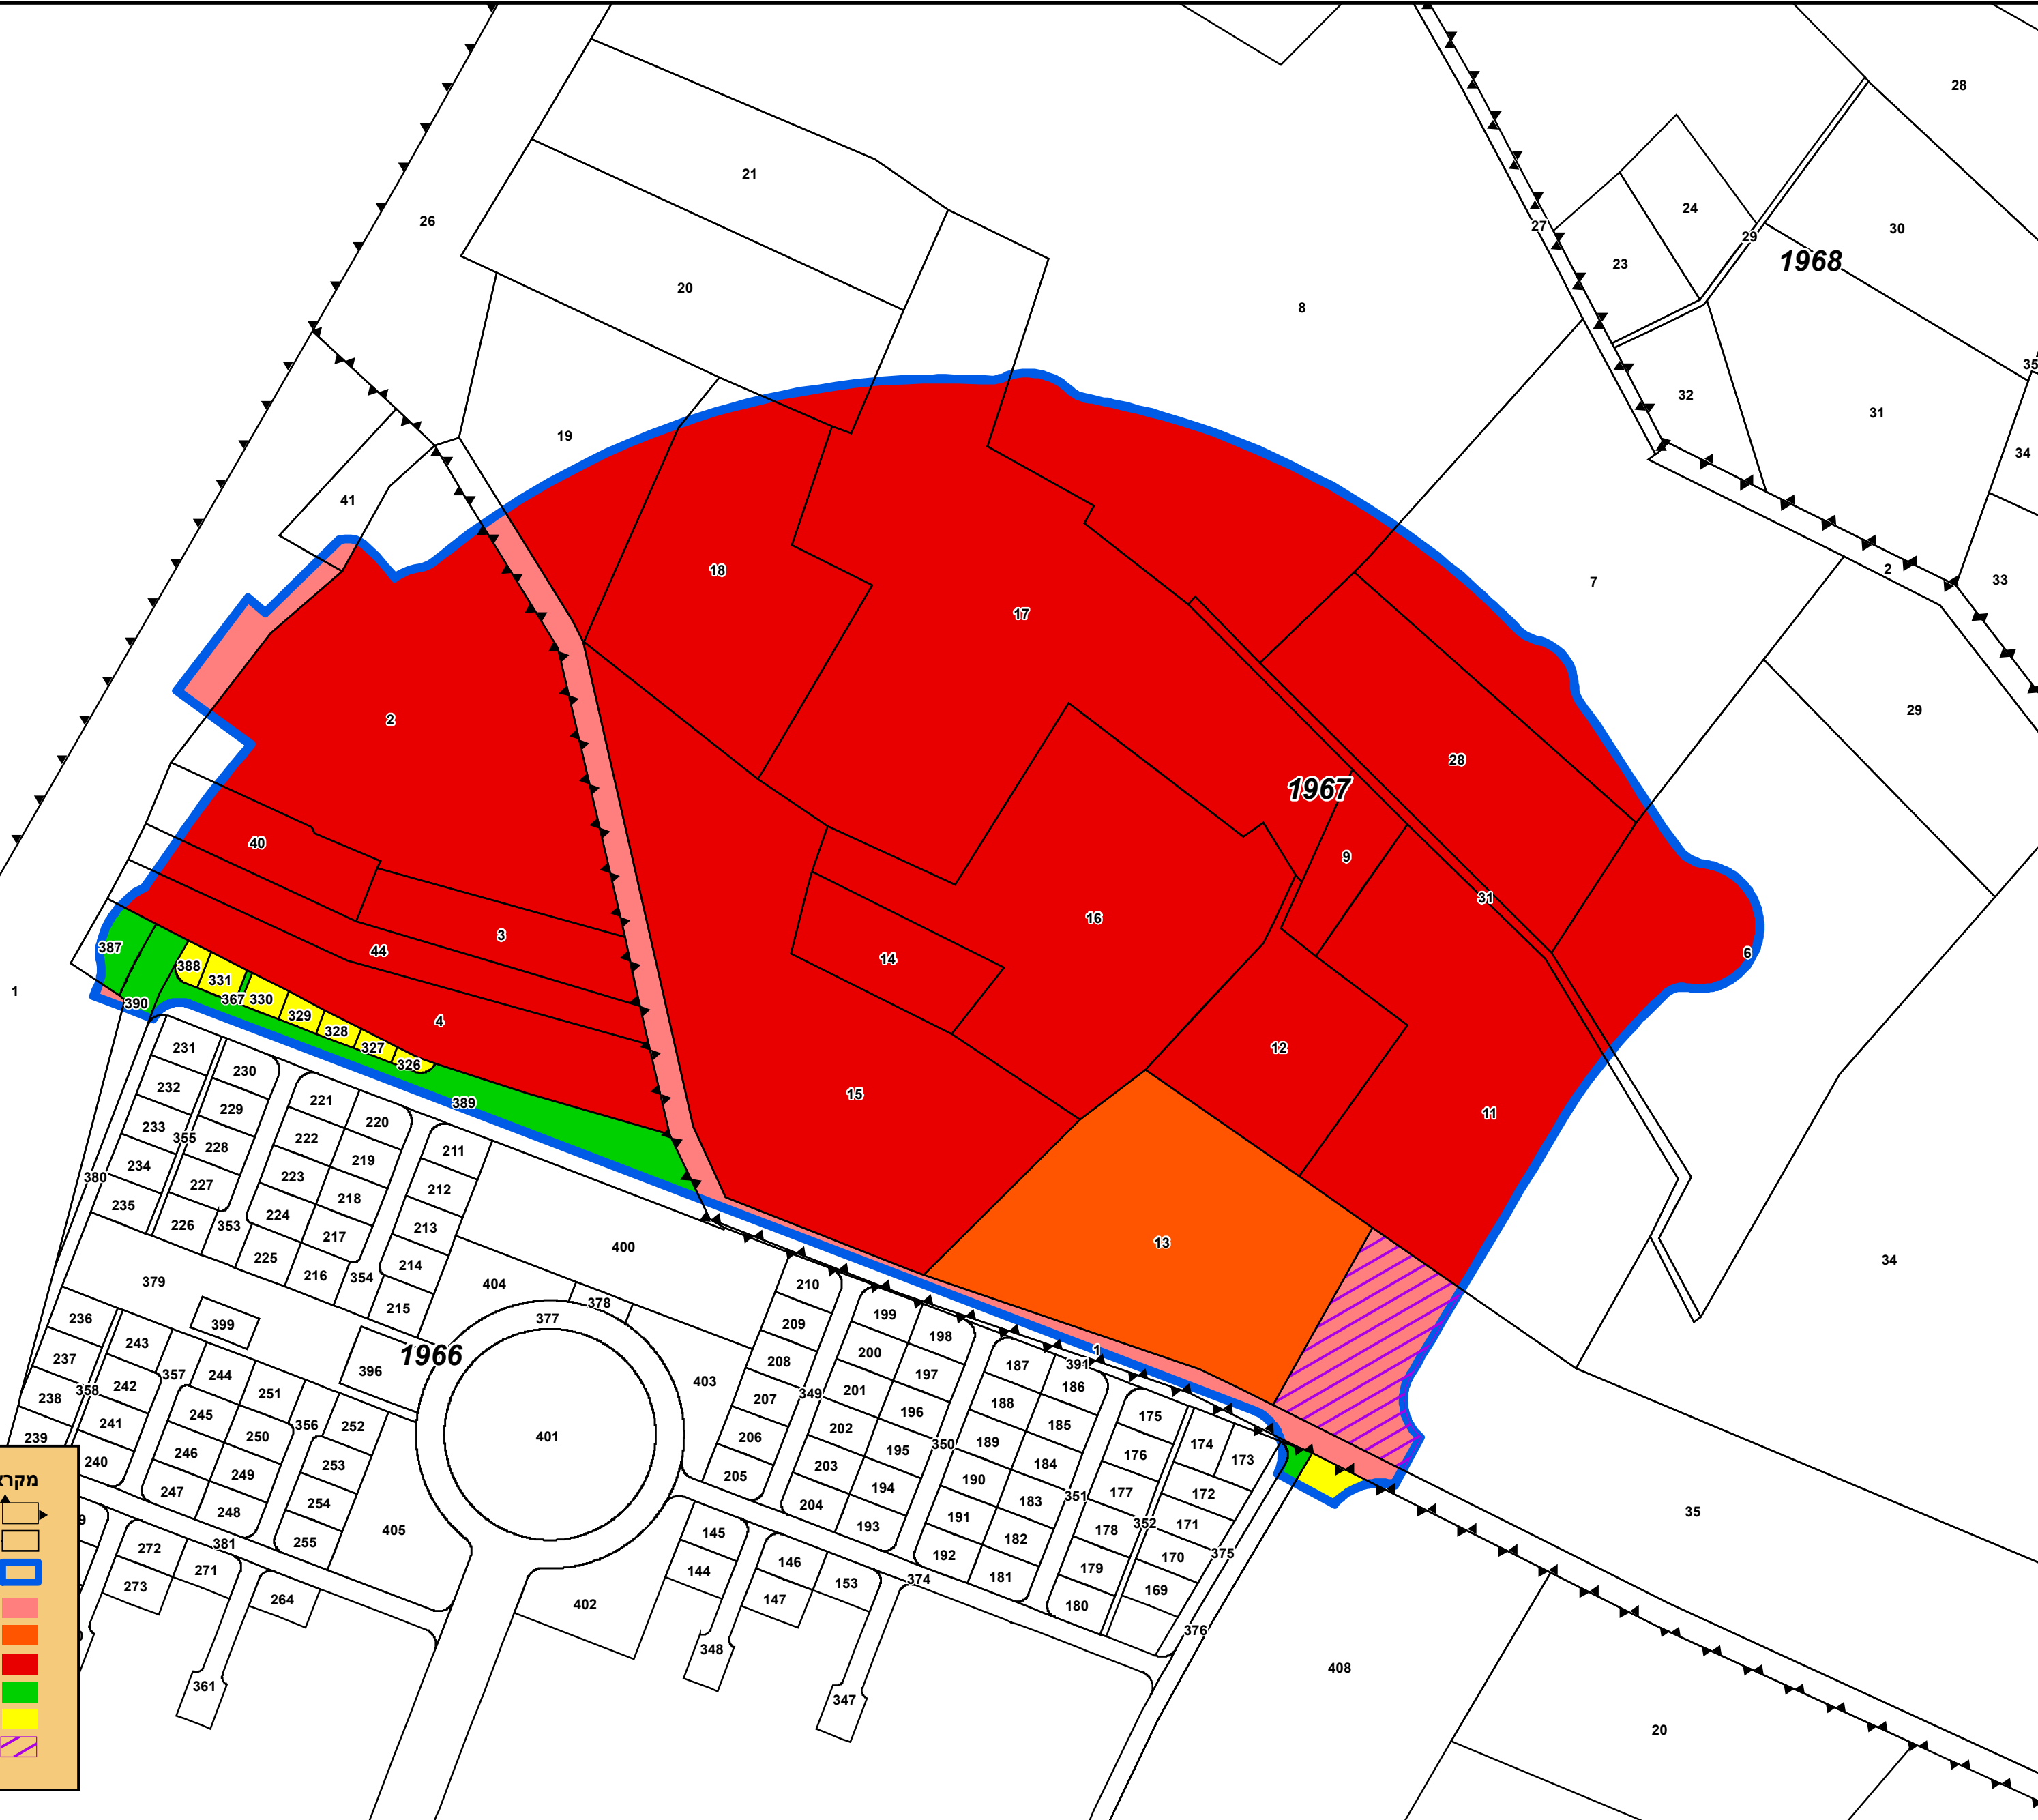

מקרא

גושים

חלקות

גבול הרשאה

מדינת ישראל

קרן קיימת לישראל

רשות הפיתוח

שלטון מקומי

פרטי

חכירות

מפת בעלויות

אתר :
הרשאה מס' :
חברה :

קנה מידה - 1:2500

טבלת שטחים

גוש	חלקה	מסדר / לא מסדר	בעלות	הערות (חכירה, משכנתא, סע' 126)
1966	1		מדינת ישראל	
1966	3		רשות הפיתוח	
1966	4		רשות הפיתוח	
1966	2		רשות הפיתוח	
1966	40		רשות הפיתוח	
1966	41		מדינת ישראל	
1966	44		רשות הפיתוח	
1966	326		פרטי	
1966	327		פרטי	
1966	328		פרטי	
1966	329		פרטי	
1966	330		פרטי	
1966	331		פרטי	
1966	367		שלטון מקומי	
1966	375		שלטון מקומי	
1966	376		שלטון מקומי	
1966	387		שלטון מקומי	
1966	388		פרטי	
1966	389		שלטון מקומי	
1966	390		שלטון מקומי	
1966	391		שלטון מקומי	
1966	408		פרטי	
1967	1		מדינת ישראל	
1967	6		רשות הפיתוח	
1967	7		רשות הפיתוח	
1967	8		רשות הפיתוח	
1967	9		רשות הפיתוח	
1967	11		רשות הפיתוח	
1967	12		רשות הפיתוח	
1967	13		קרן קיימת לישראל	
1967	14		רשות הפיתוח	
1967	15		רשות הפיתוח	
1967	16		רשות הפיתוח	
1967	17		רשות הפיתוח	
1967	18		רשות הפיתוח	
1967	19		רשות הפיתוח	
1967	20		רשות הפיתוח	
1967	28		רשות הפיתוח	
1967	31		רשות הפיתוח	
1967	35		מדינת ישראל	

הוכן ע"י : _____ תאריך : _____

המידע שבמפה מבוסס על נסחי רישום עדכניים מיום : _____

חתימת החברה : _____ תאריך : _____