


מספר סידורי : 303171

משרד הבינוי והשיכון
2634/2017
המרכז למיפוי ישראל

תת"ג לגוש בהסדר

מחוז : תל אביב
נפה : תל אביב
מקום : תל אביב
גוש : 8836
חלקות: 11

הוכן עבור: מרכז למיפוי ישראל

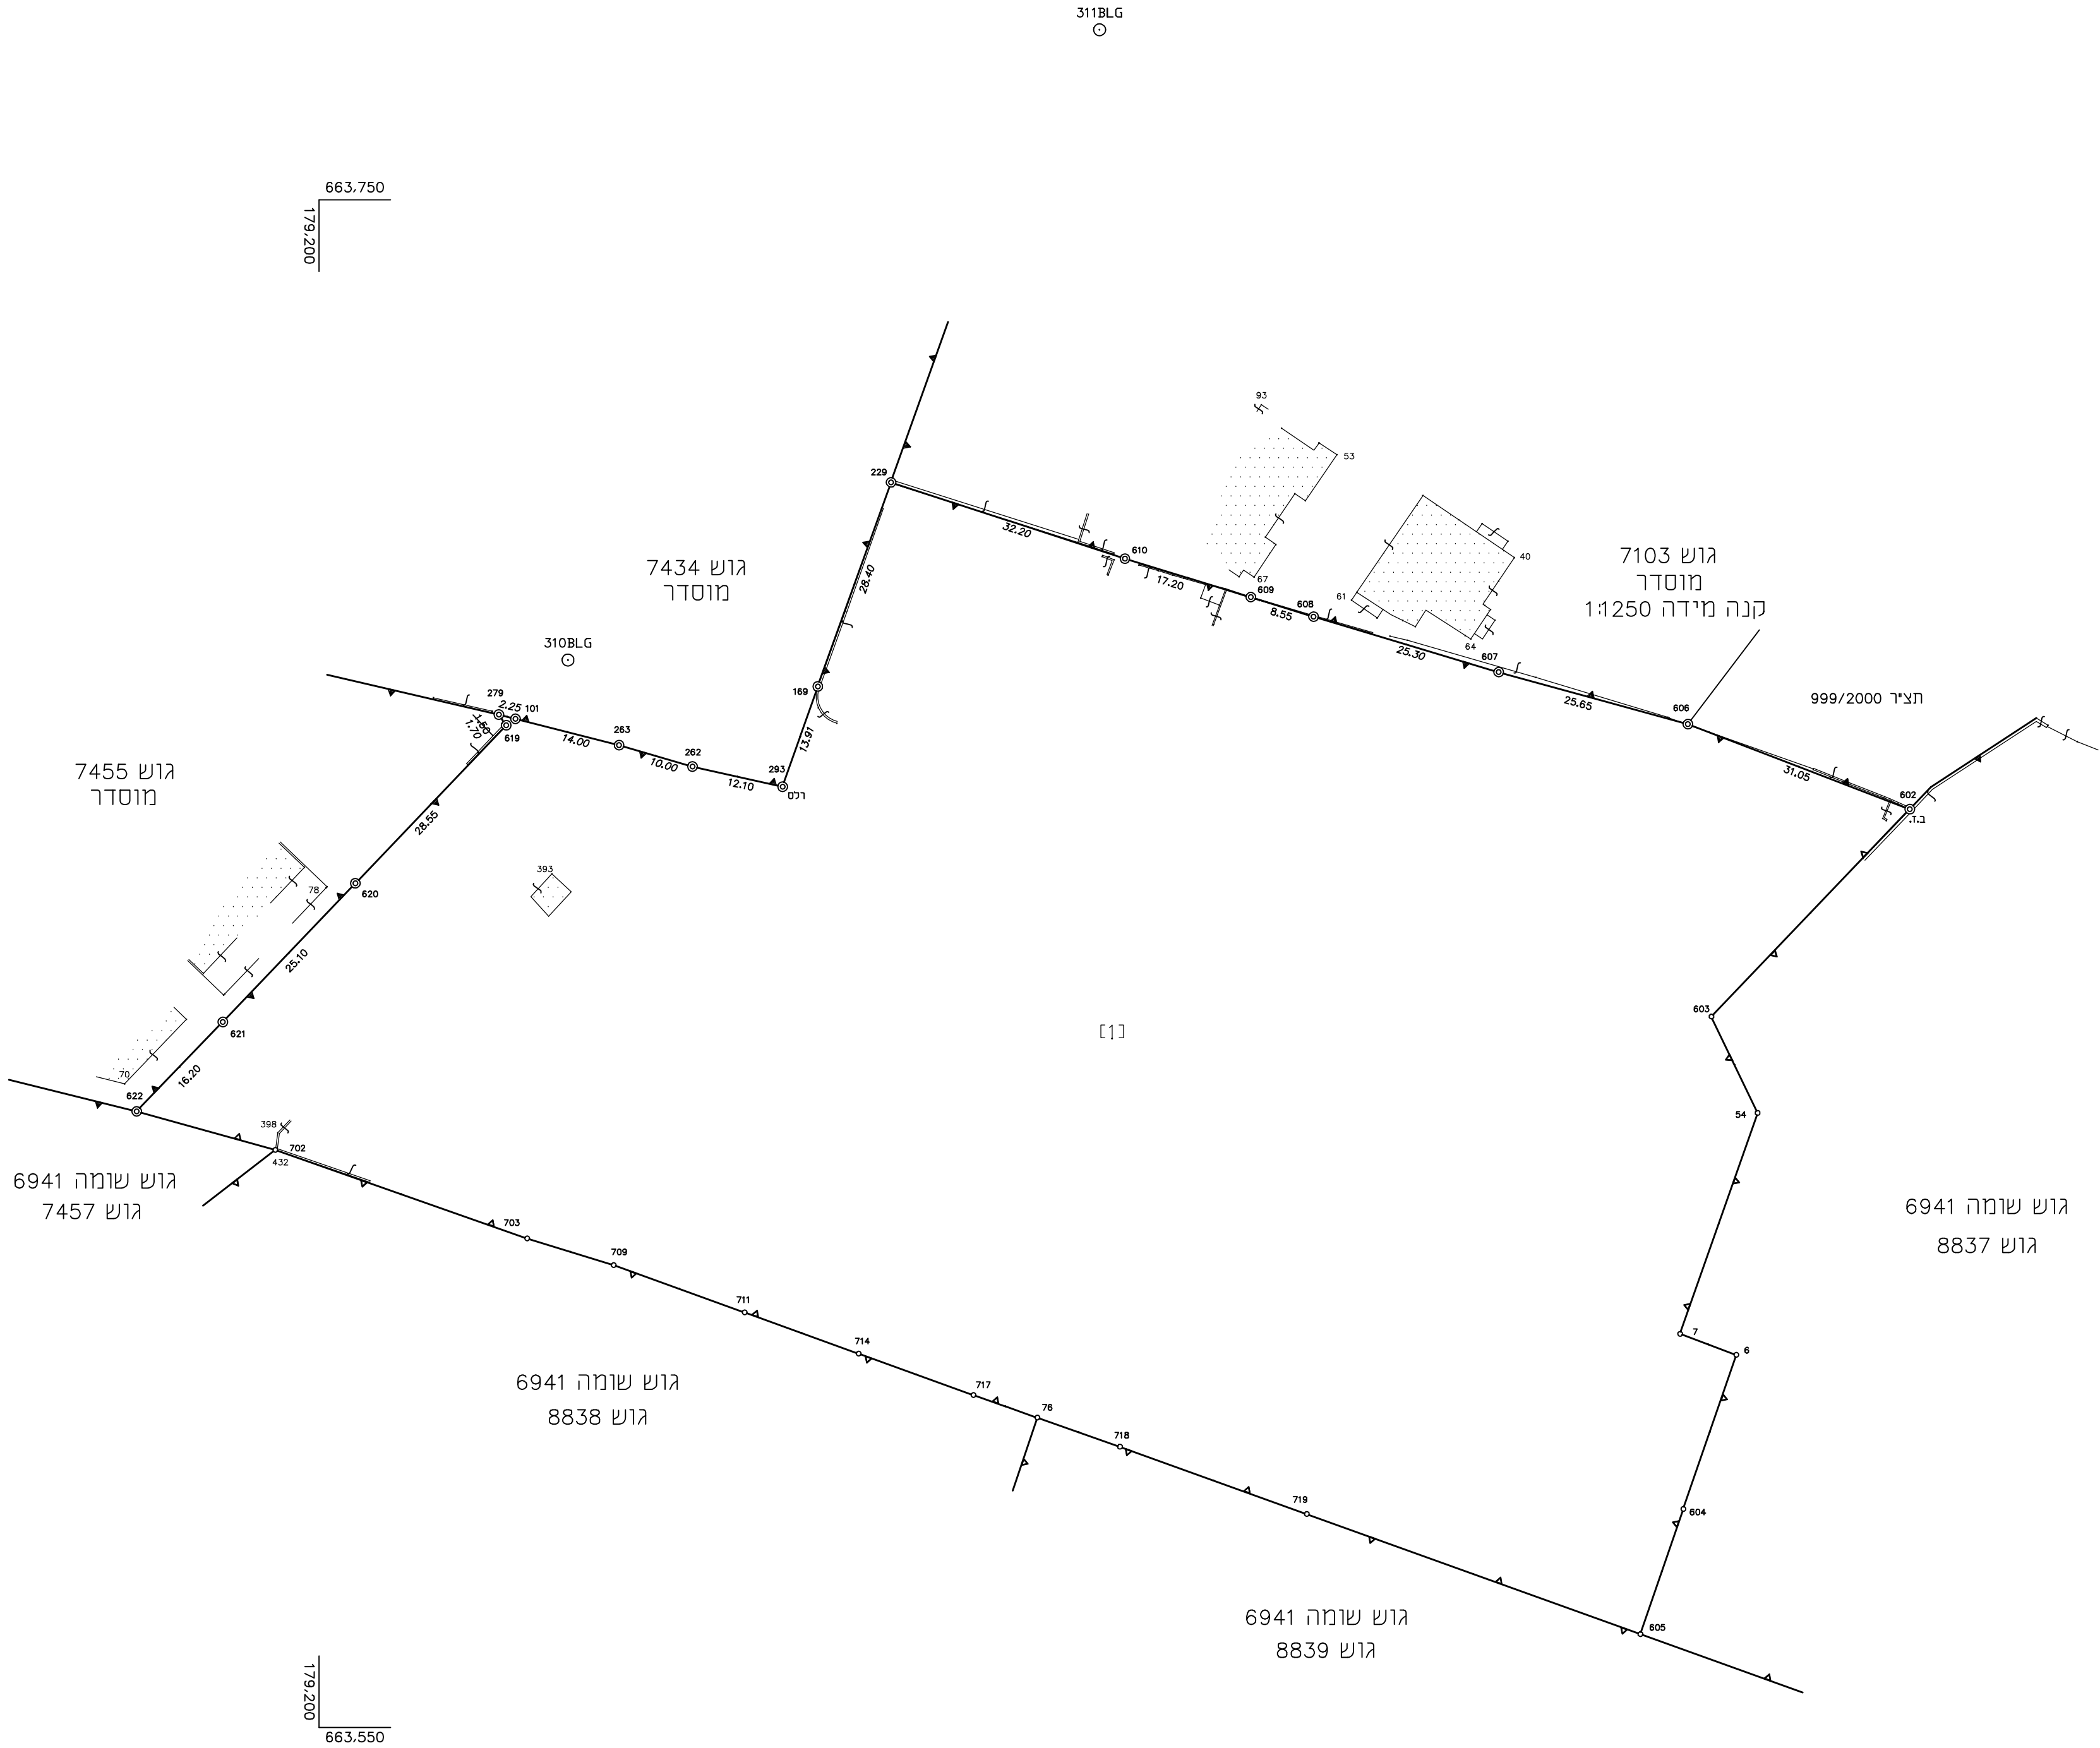

טבלת שטחים

מספר חקלא	שטח רשום	שטח מושב	הכ"ש	עומד
11	18.487	18.484	0.003	חקר

התשרים נבדק על-ידי ונמצא תקין ,
אני ממליץ למפי לאשרו ככשר לתעוד גבולות
חתימה:.....תאריך:.....

אני מאשר בזה כי תשרים זה מתאר בדיוק את מצבם וגבולותיהם של המקומות המוזכרים
בו במועדים המצוינים להלן:

תאריך מדידת הפרטים : 10.08.17
תאריך מדידת סימני הגבול הישנים שנמצאו או שחזרו בשדה :
תאריך מדידת סימני הגבול האחרים אם סומנו ונמדדו :
.....

אני מאשר בזה כי ערכתי את התחילי לפי תקנות המדידות
מדידות ומיפוי, התשע"ז - 2016, וכי הוא ראוי לאישור לתיעוד גבולות

תאריך גמר התכנית : 30.10.2017
המקום :
.....

ישראל ישראל
שם המודד ומענו
מספר רשיון
חתימה



- הערות :
- התכנית מבוססת על מפות גוש רישום מספר 7103.7334.7455.
 - כל נסודות הגבול שלא תוארו אינו מסומנות בשטח.
 - כל הגבולות שלא תוארו אחרת הם מסוג בלתי מסוגל.
 - כל הגבולות עם גושים לא מוסדרים אינם סופיים ועלולים להשתנות בעת הליך ההסדר.