גוש רישום 12223   השטח 23.309 דונם   חיפה   מחוז חיפה   נפת חיפה   קנה מידה 1 : 625

מפה סופית

גיליון 1 מתוך 2

מספר החלקה	שטח בדונמים
1	0. 597
2	0. 581
3	0. 318
4	0. 519
5	0. 664
6	3. 340
7	1. 194
8	0. 042
9	0. 047
10	1. 732
11	0. 369
12	0. 327
13	1. 582
14	2. 961
15	0. 744
16	0. 587
17	0. 242
18	0. 386
19	1. 604
20	0. 940
21	0. 932
22	2. 378
23	0. 121
24	0. 359
25	0. 532
26	0. 211

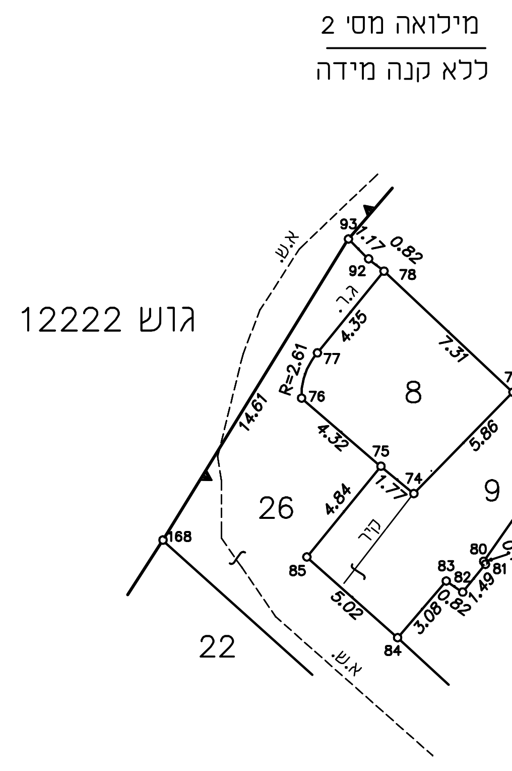

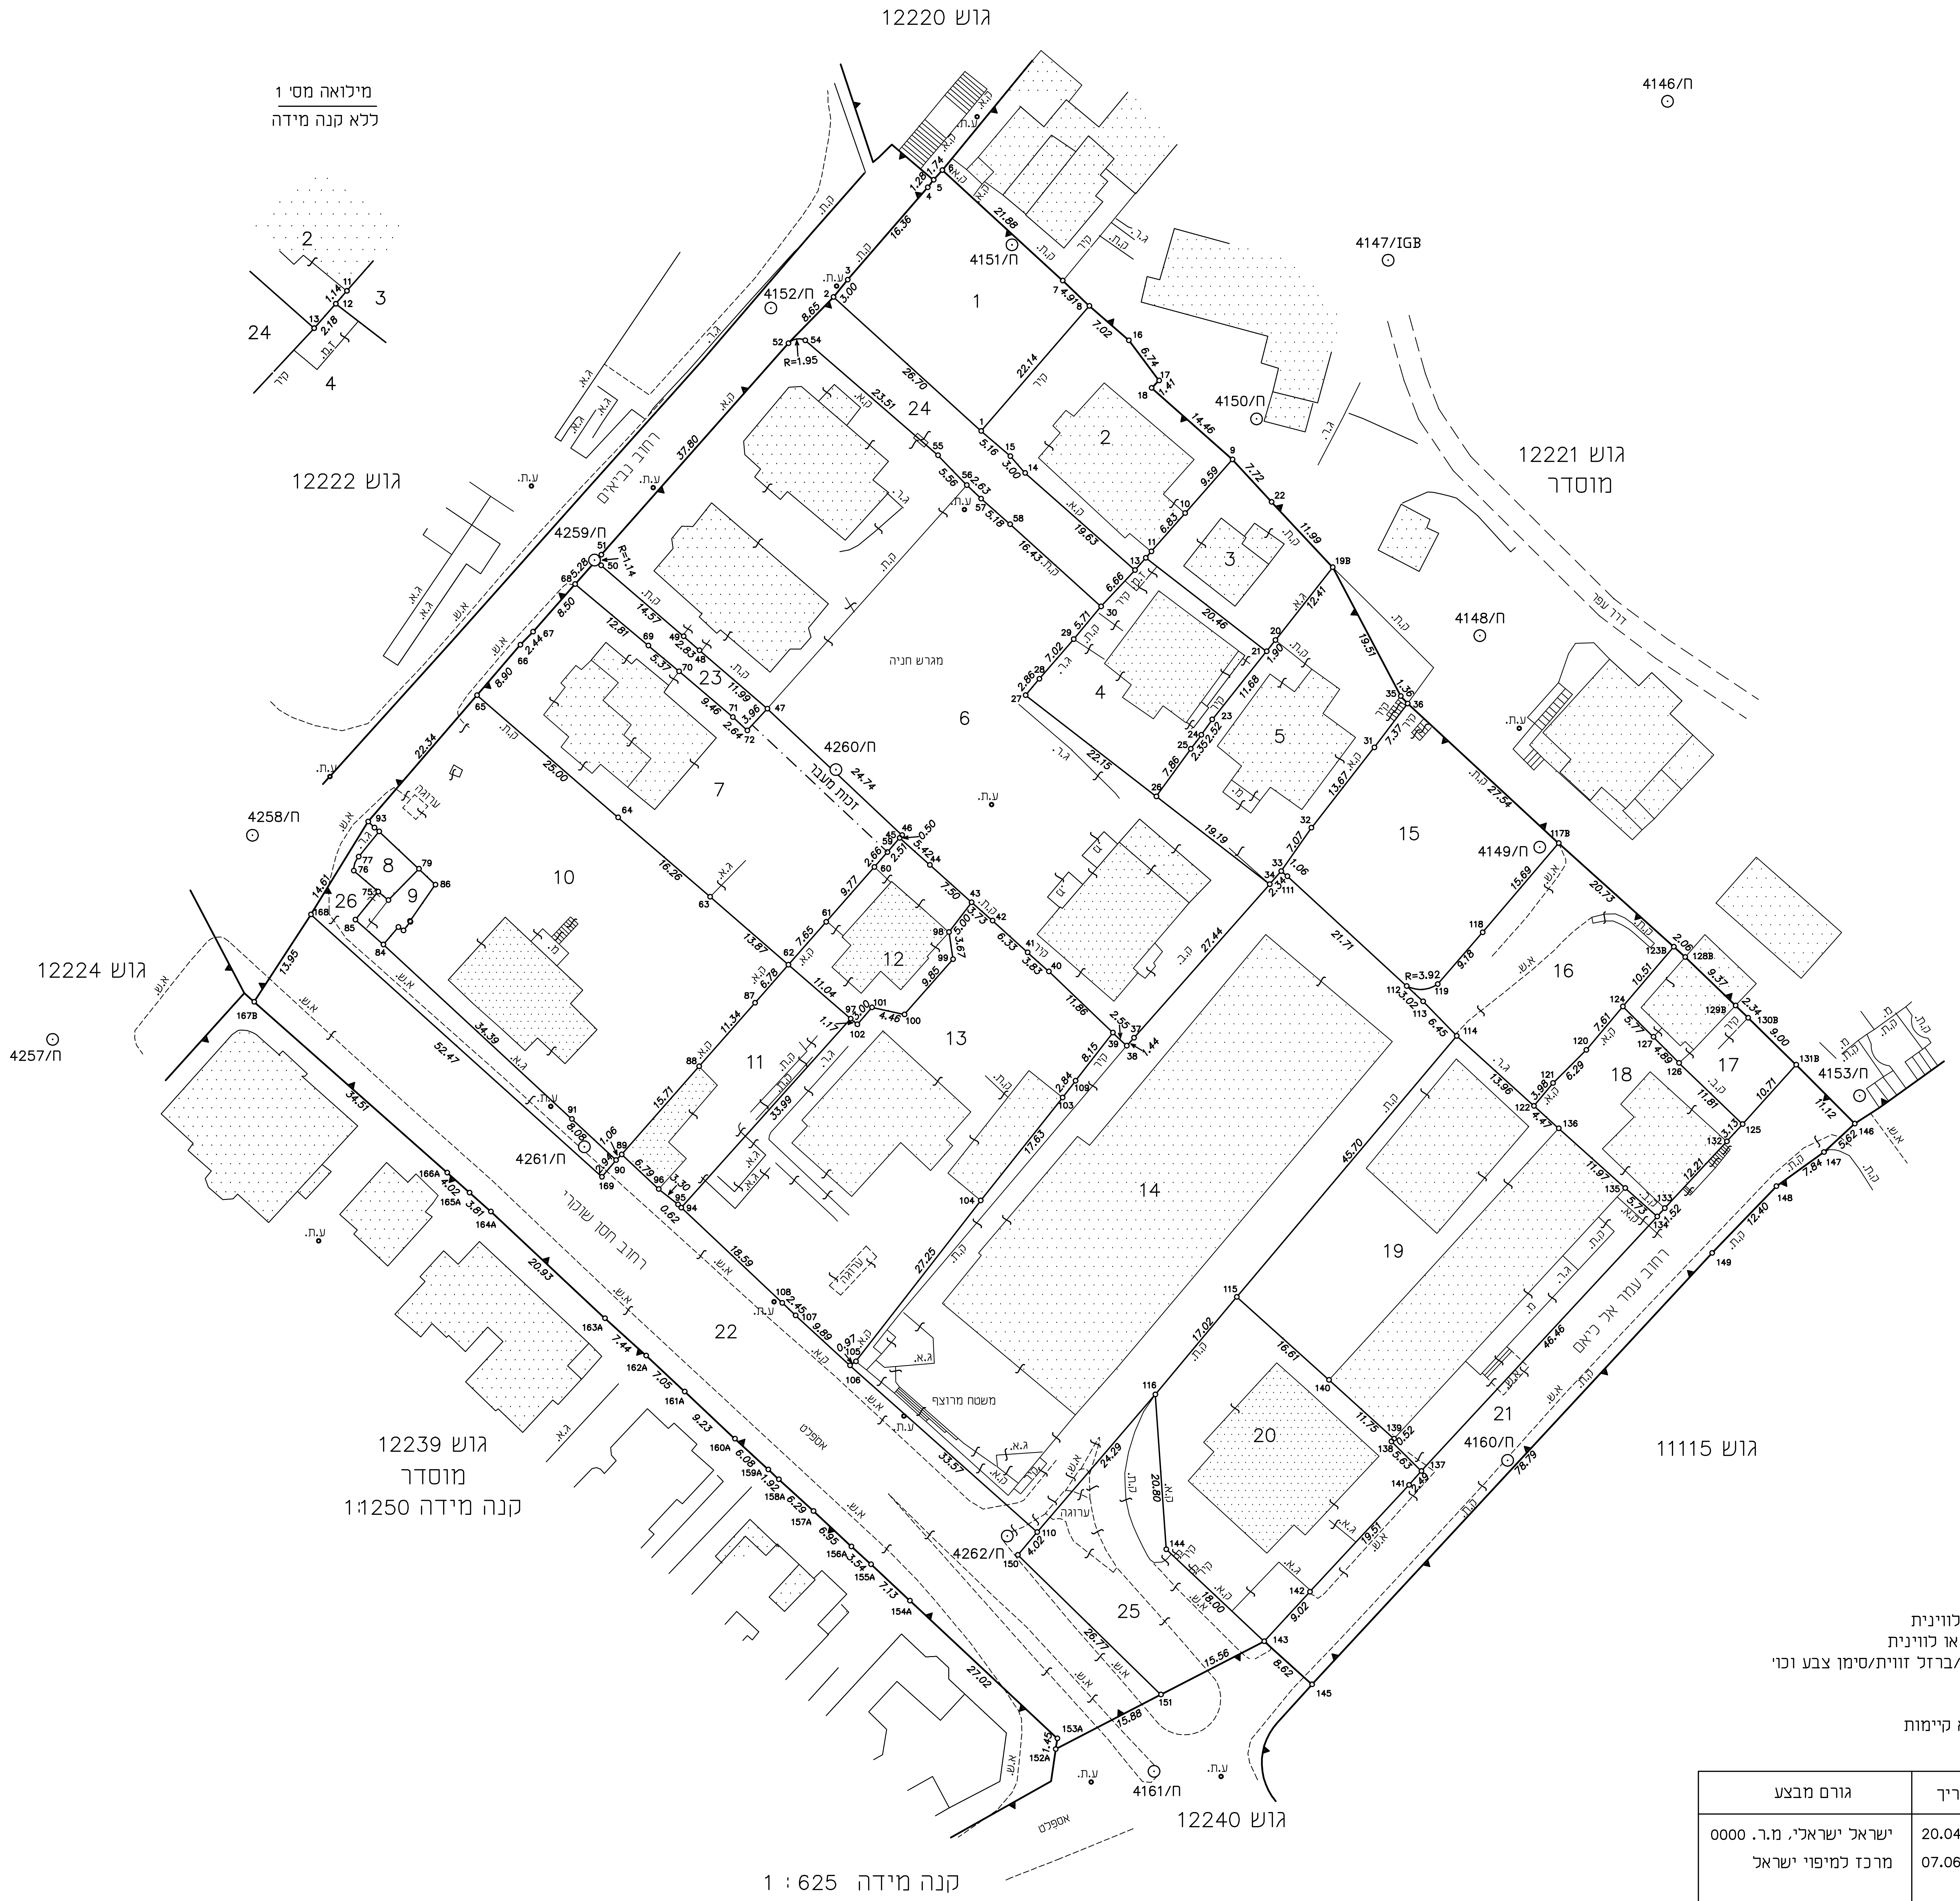

קנה מידה 1 : 625

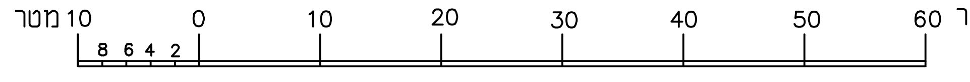

הערות :

1. המדידה בוצעה ברשת ישראל 2005/12
2. שיטת מדידת הפרטים : פוטוגרמטריה, קוטבית או לווינית
3. שיטת מדידת הגבולות ופרטים להתמרה : קוטבית או לווינית
4. כל הגבולות ללא סיווג סימון הם מסוג : לא סומנו/ברזל זווית/סימן צבע וכו׳
5. גוש/י השומה בתחום גוש ההסדר : לא קיימים
6. מספר/י התצ״ר בתחום גוש ההסדר : לא קיימות
7. מספר/י תכניות מאושרות שחלות בתחום הגוש לא קיימות
8. עדכונים במפה :

מספר עדכון	תיאור העדכון	תאריך	גורם מבצע
1	הכנה מפה סופית	20.04.2018	ישראל ישראלי, מ.ר. 0000
2	ביקורת מפה סופית	07.06.2018	מרכז למיפוי ישראל

המרכז למיפוי ישראל, סיוון תשע"ח - יוני 2018
כל זכויות ההעתקה שמורות