3/4/282/תח'

תשריט איחוד וחלוקת מגרשים בהסכמת הבעלים

מחוז : מרכז
נפה : רחובות
מקום : **חפץ חיים**
גוש : 5449
חלקי חלקות : 6
גוש : 4729
חלקי חלקות : 3
מגרשים : 601 ,600
עפ"י תב"ע : בר/4/282
שטח התכנית : 55.465 ד'
הוכן עבור : קיבוץ חפץ חיים
קנה מידה : 1 : 1000

הועדה המקומית
לתכנון ובניה "שורקות"
03-10-2010
נתקבל
חתימה

הועדה המקומית לתכנון ולבניה "שורקות"
תכנית אחוד ו/או חלוקה מס' תח/282/4/3'
תואם לת/מ מס' בר/282/4 **בתוקף מיום**
ישיבת מליאה מס' 2010009 **מיום** 26/10/2010
הוחלט לאשר את התשריט
ציון רבי
יו"ר הועדה
איגנ' אנה סוגן
מהנדסת הועדה
21/11/2010
תאריך

מס' סידורי : ג.ב. / 10/492
ורסיה 1
תאריך : 03-08-2010

תרשים סביבה 1 : 5000

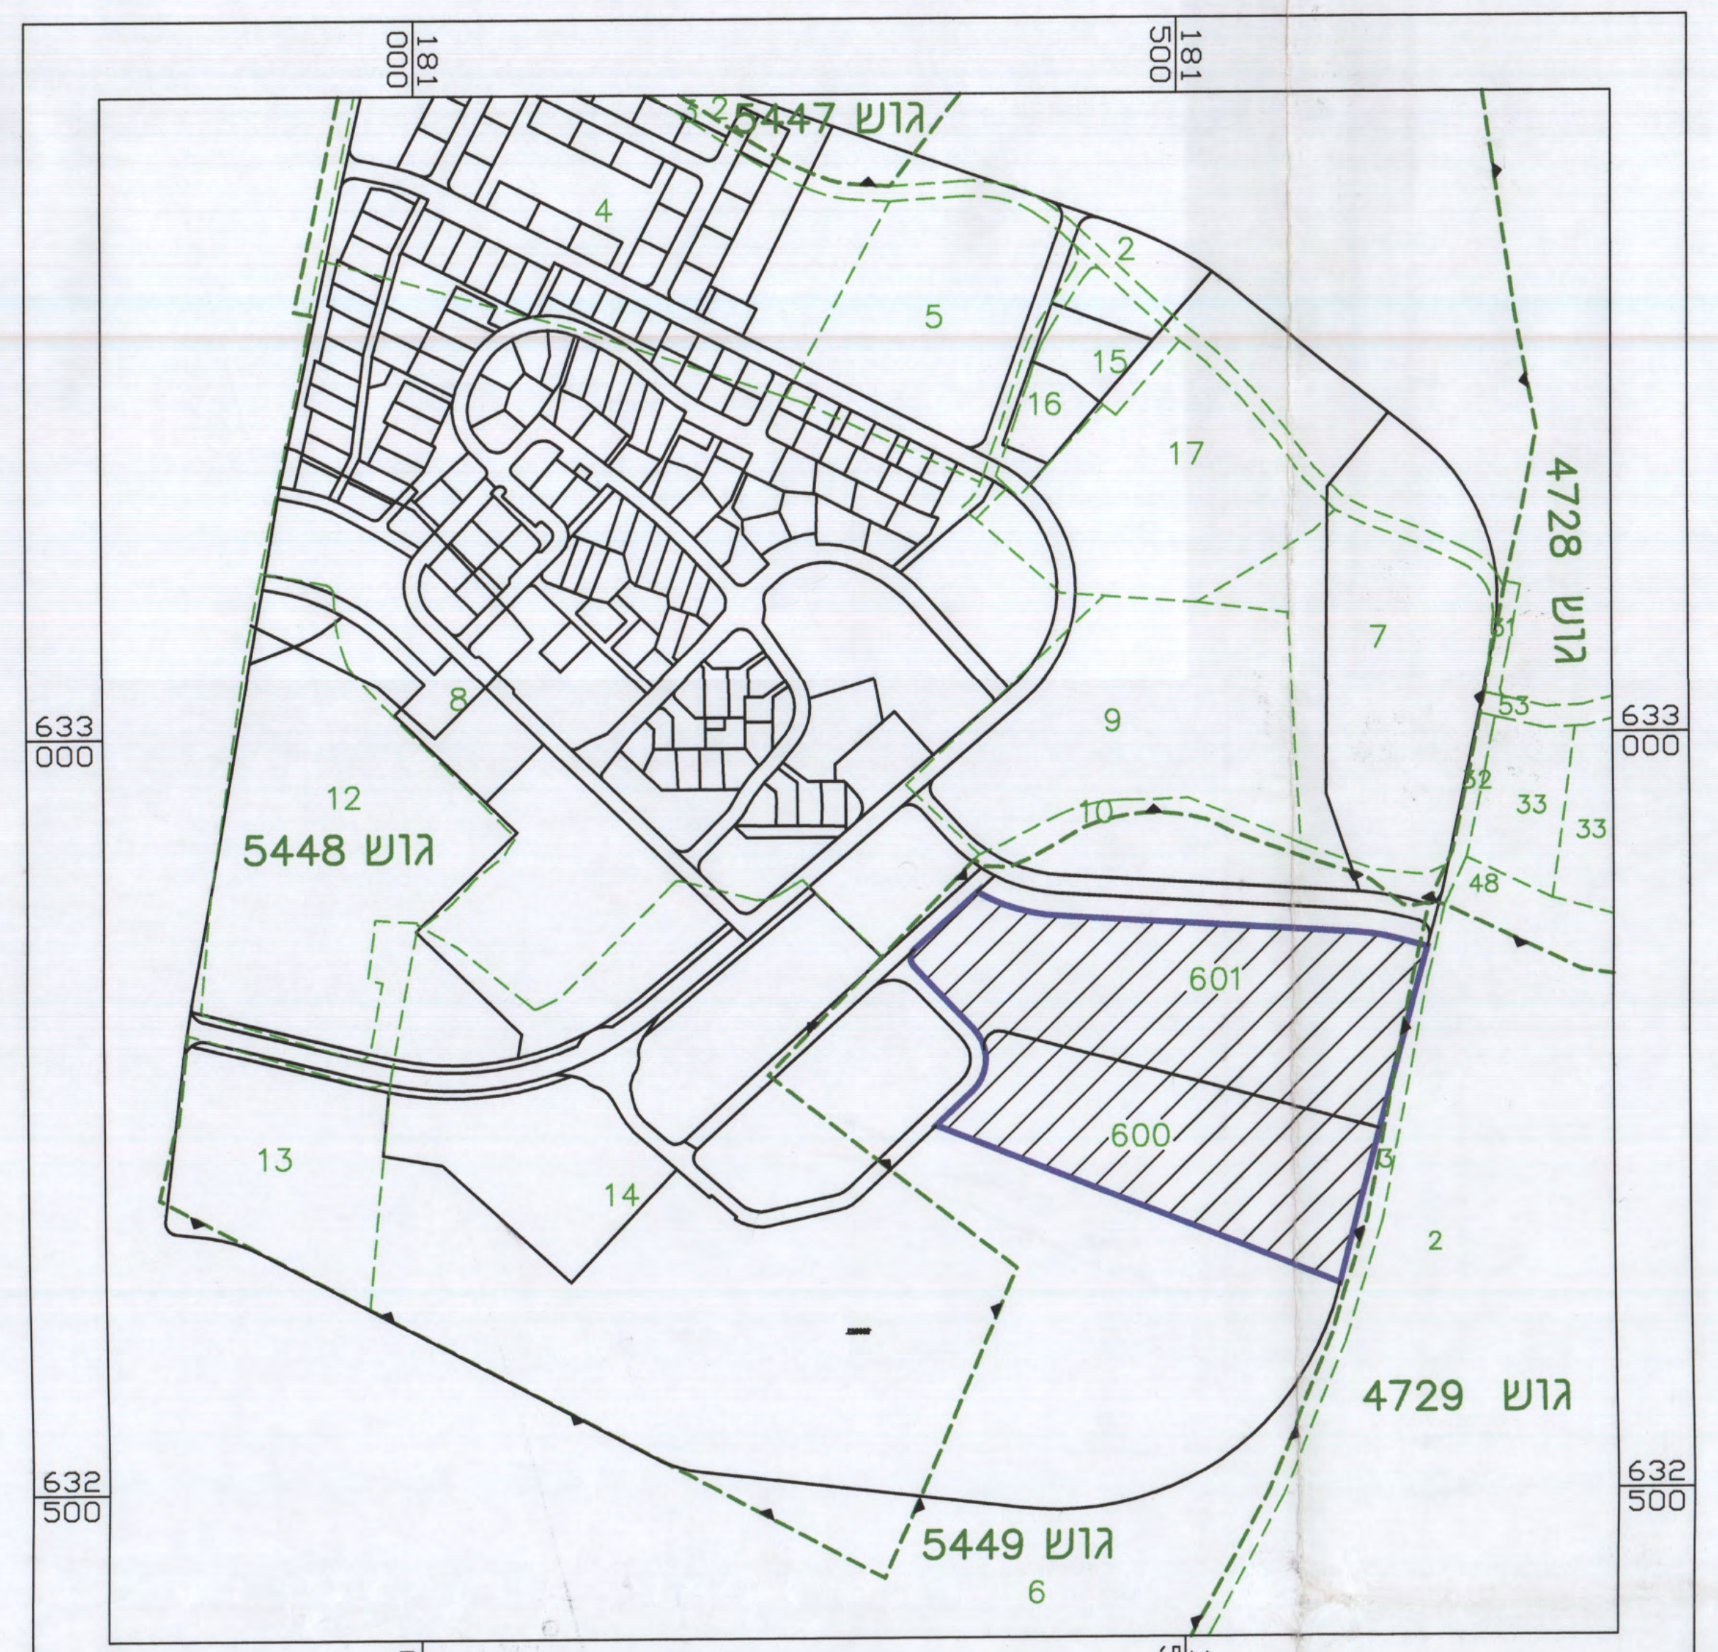

טבלת שטחים

מצב קיים			מצב מוצע		
יעוד	מס' מגרש	השטחים בדונמים	יעוד	מס' מגרש	השטחים בדונמים
תעשיה	600	23.960	תעשיה	600A	31.251
תעשיה	601	31.505	תעשיה	601A	24.214
	סה"כ	55.465		סה"כ	55.465

מקרא :

גבול תוכנית	▬
גבול גוש רשום	- - ▼ - - ▲ - -
גבול חלקה רשומה	- - - - - -
מפוי מצבי	─
גבול מגרש \ יעוד	▬
מס' חלקה רשומה	⑥
מס' תא שטח קיים/ מוצע	600

הערות :

1. גבולות החלקות התקבלו מתכנית לצרכי רישום של ג.ב. 08/521/7.
2. גבולות המגרשים התקבלו עפ"י הסכם בין חפץ חיים לגני טל.

אין לנו התנגדות עקרונית לתוכנית, בתנאי שזו תהיה מתואמת עם רשויות התכנון המוסמכות.
חתימתנו הינה לצרכי תכנון בלבד, אין בה כדי להקנות כל זכות ליוזם התכנית או לכל בעל עניין אחר בשטח התכנית כל עוד לא הוקצה השטח ונחתם עמנו הסכם מתאים בגינו ואין חתימתנו זו באה במקום הסכמת כל בעל זכות בשטח הנדון ו/או כל רשות מוסמכת, לפי כל חוזה חתום ועפ"י כל דין.
למען הסר ספק מוצהר בזה כי אם נעשה או ייעשה על ידינו הסכם בגין השטח הכלול בתכנית, אין בחתימתנו על התכנית הודאה בקיום הסכם כאמור ו/או ויתור על זכותנו לבטלו בגין הפרתו ע"י מי שרכש מאתנו על פיו זכויות בשטח, ו/או על כל זכות אחרת העומדת לנו מכח הסכם כאמור ועפ"י כל דין, שכן חתימתנו ניתנת אך ורק מנקודת מבט תכנונית.
מינהל מקרקעי ישראל
מחוז המרכז
19 AUG 2010

מנהל תחום
מינהל מקרקעי ישראל
מחוז המרכז

קיבוץ חפץ חיים
מקוצת פועלים
להתישבות שיתופית בע"מ

מועצה אזורית
נחל שורק

גני טל החדשה
מושב עובדים להתיישבות
חקלאית שיתופית בע"מ

לא לצרכי רישום
גטניו ברני מודד מוסמך
רשיון מס' 570
חתימה
תאריך : 03-08-2010

גטניו ושות'
מודדים מוסמכים בע"מ
רח' הירקון 67, בני-ברק 51206 טל. 03-7541000 פקס. 03-7516356

P:\2010\100506\register\tasrit haluka\index_100506.dwg

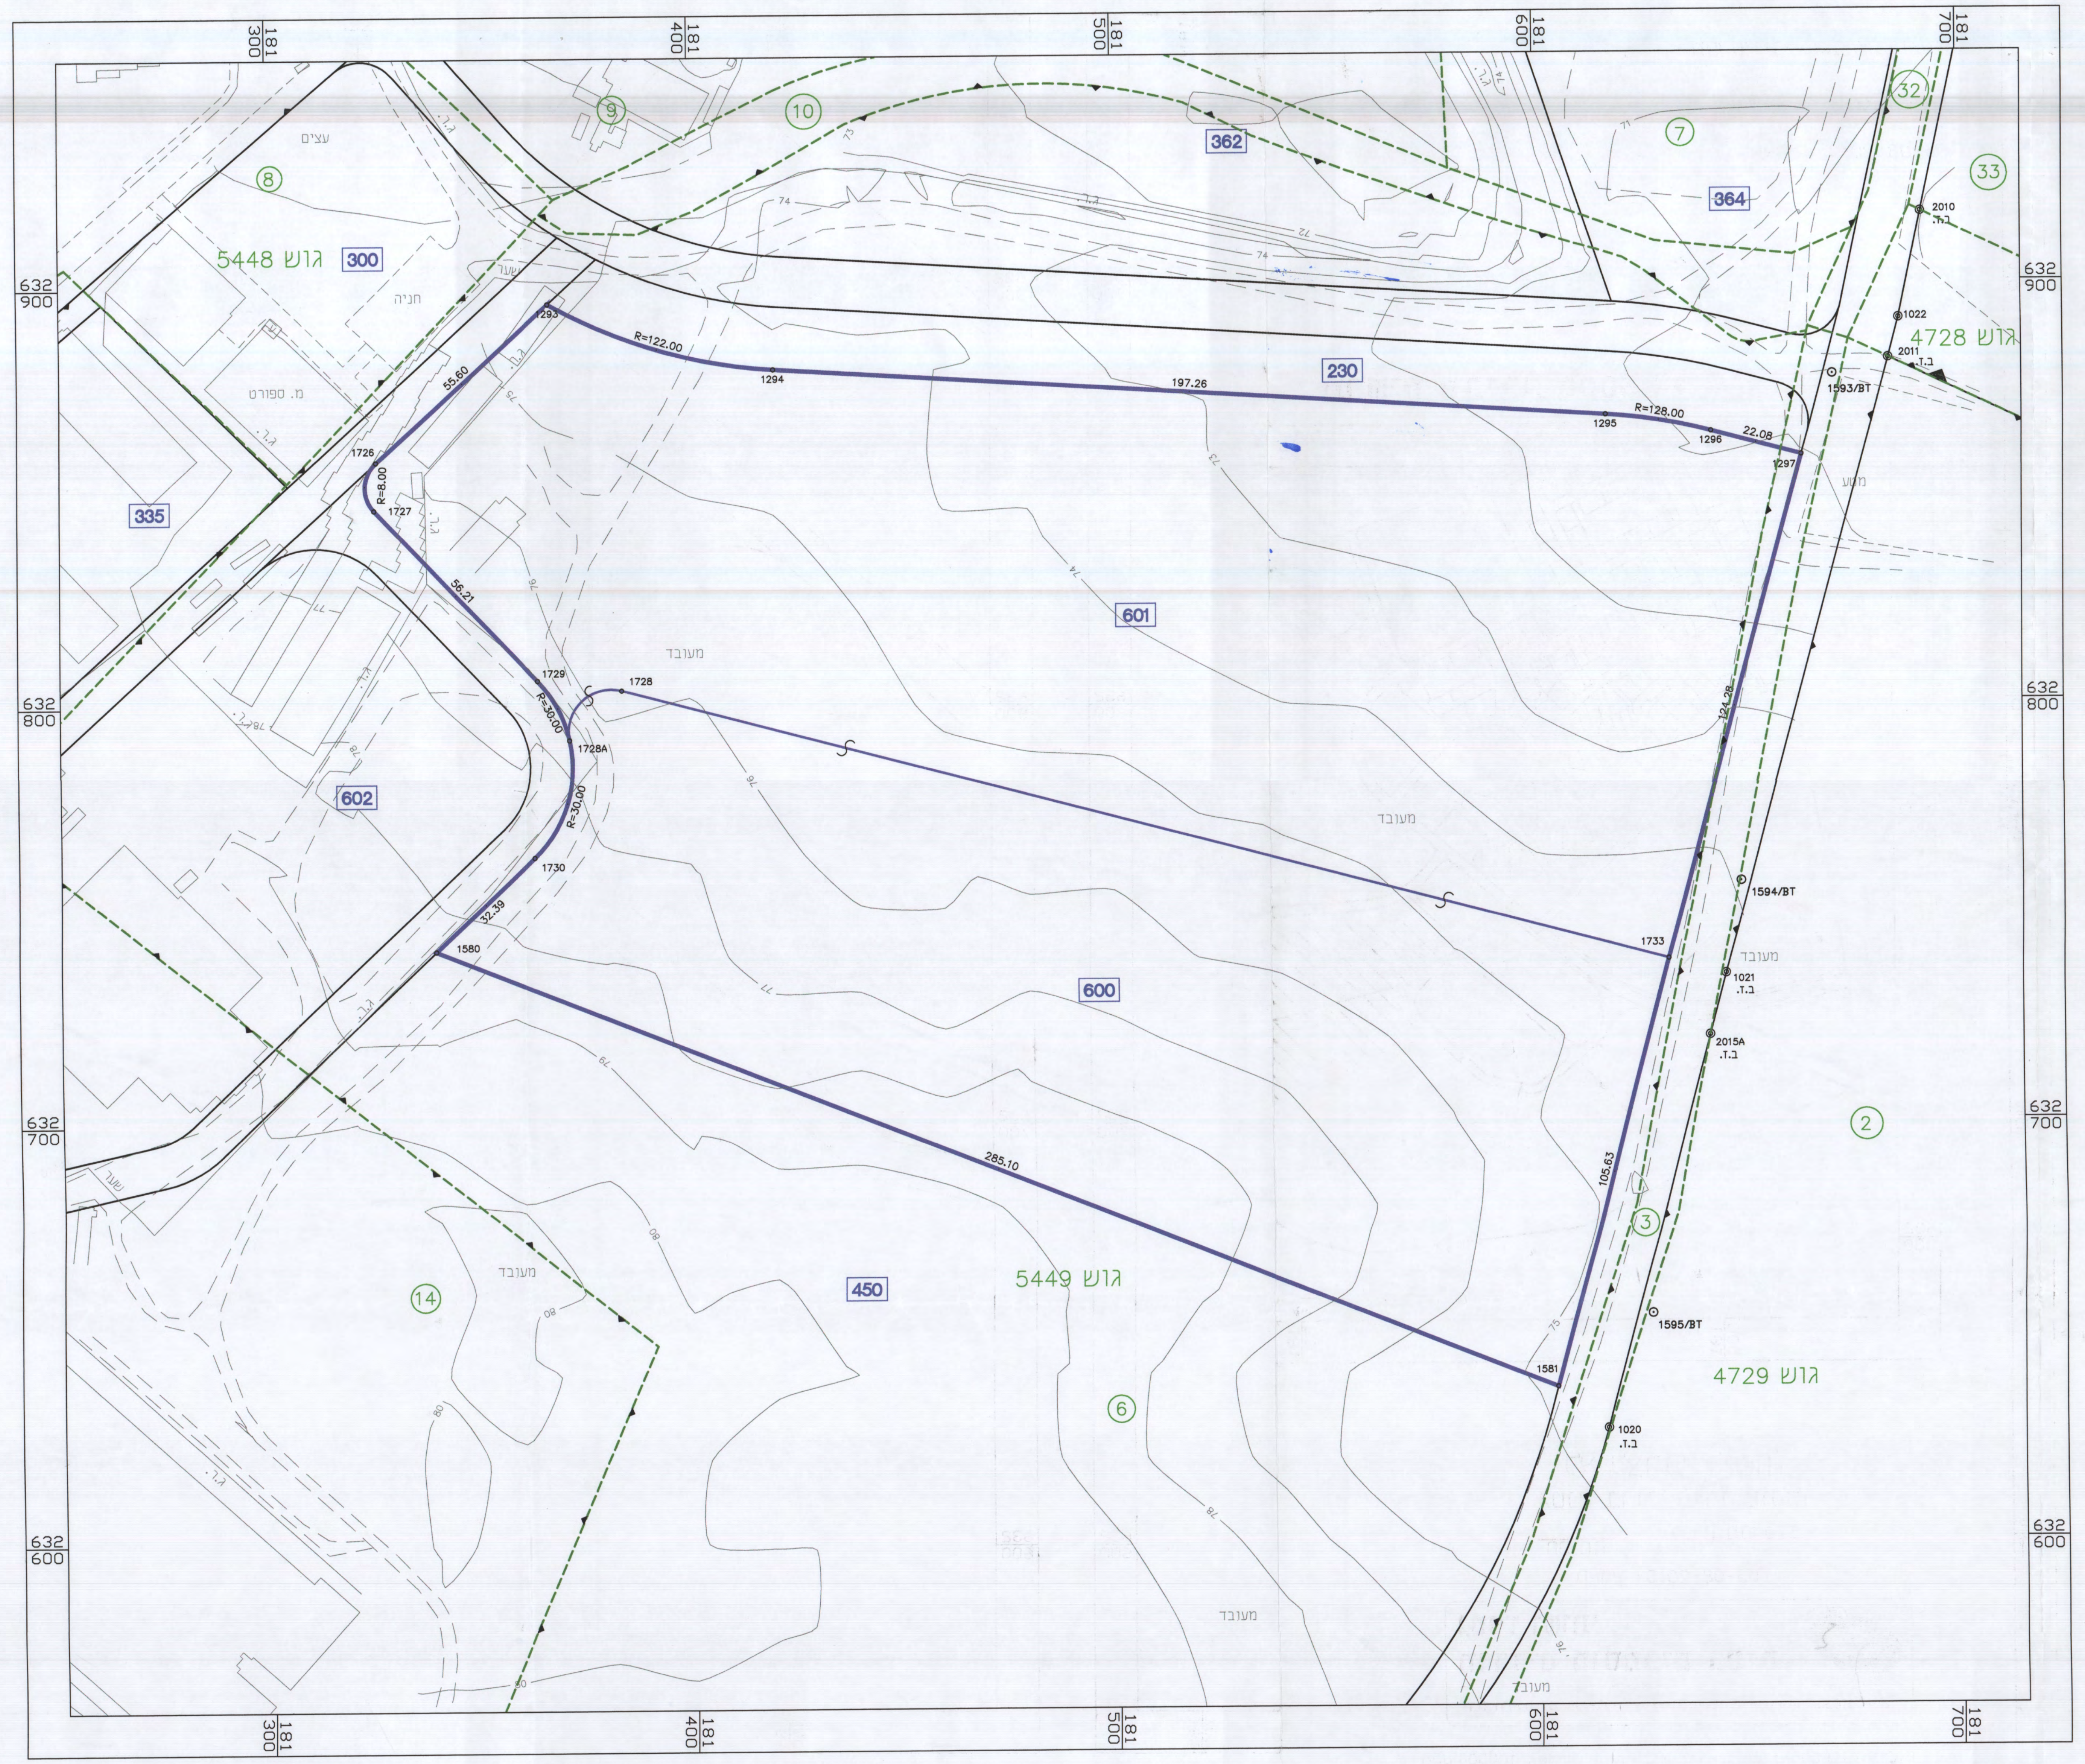

מצב מאושר קנ"מ 1 : 1000

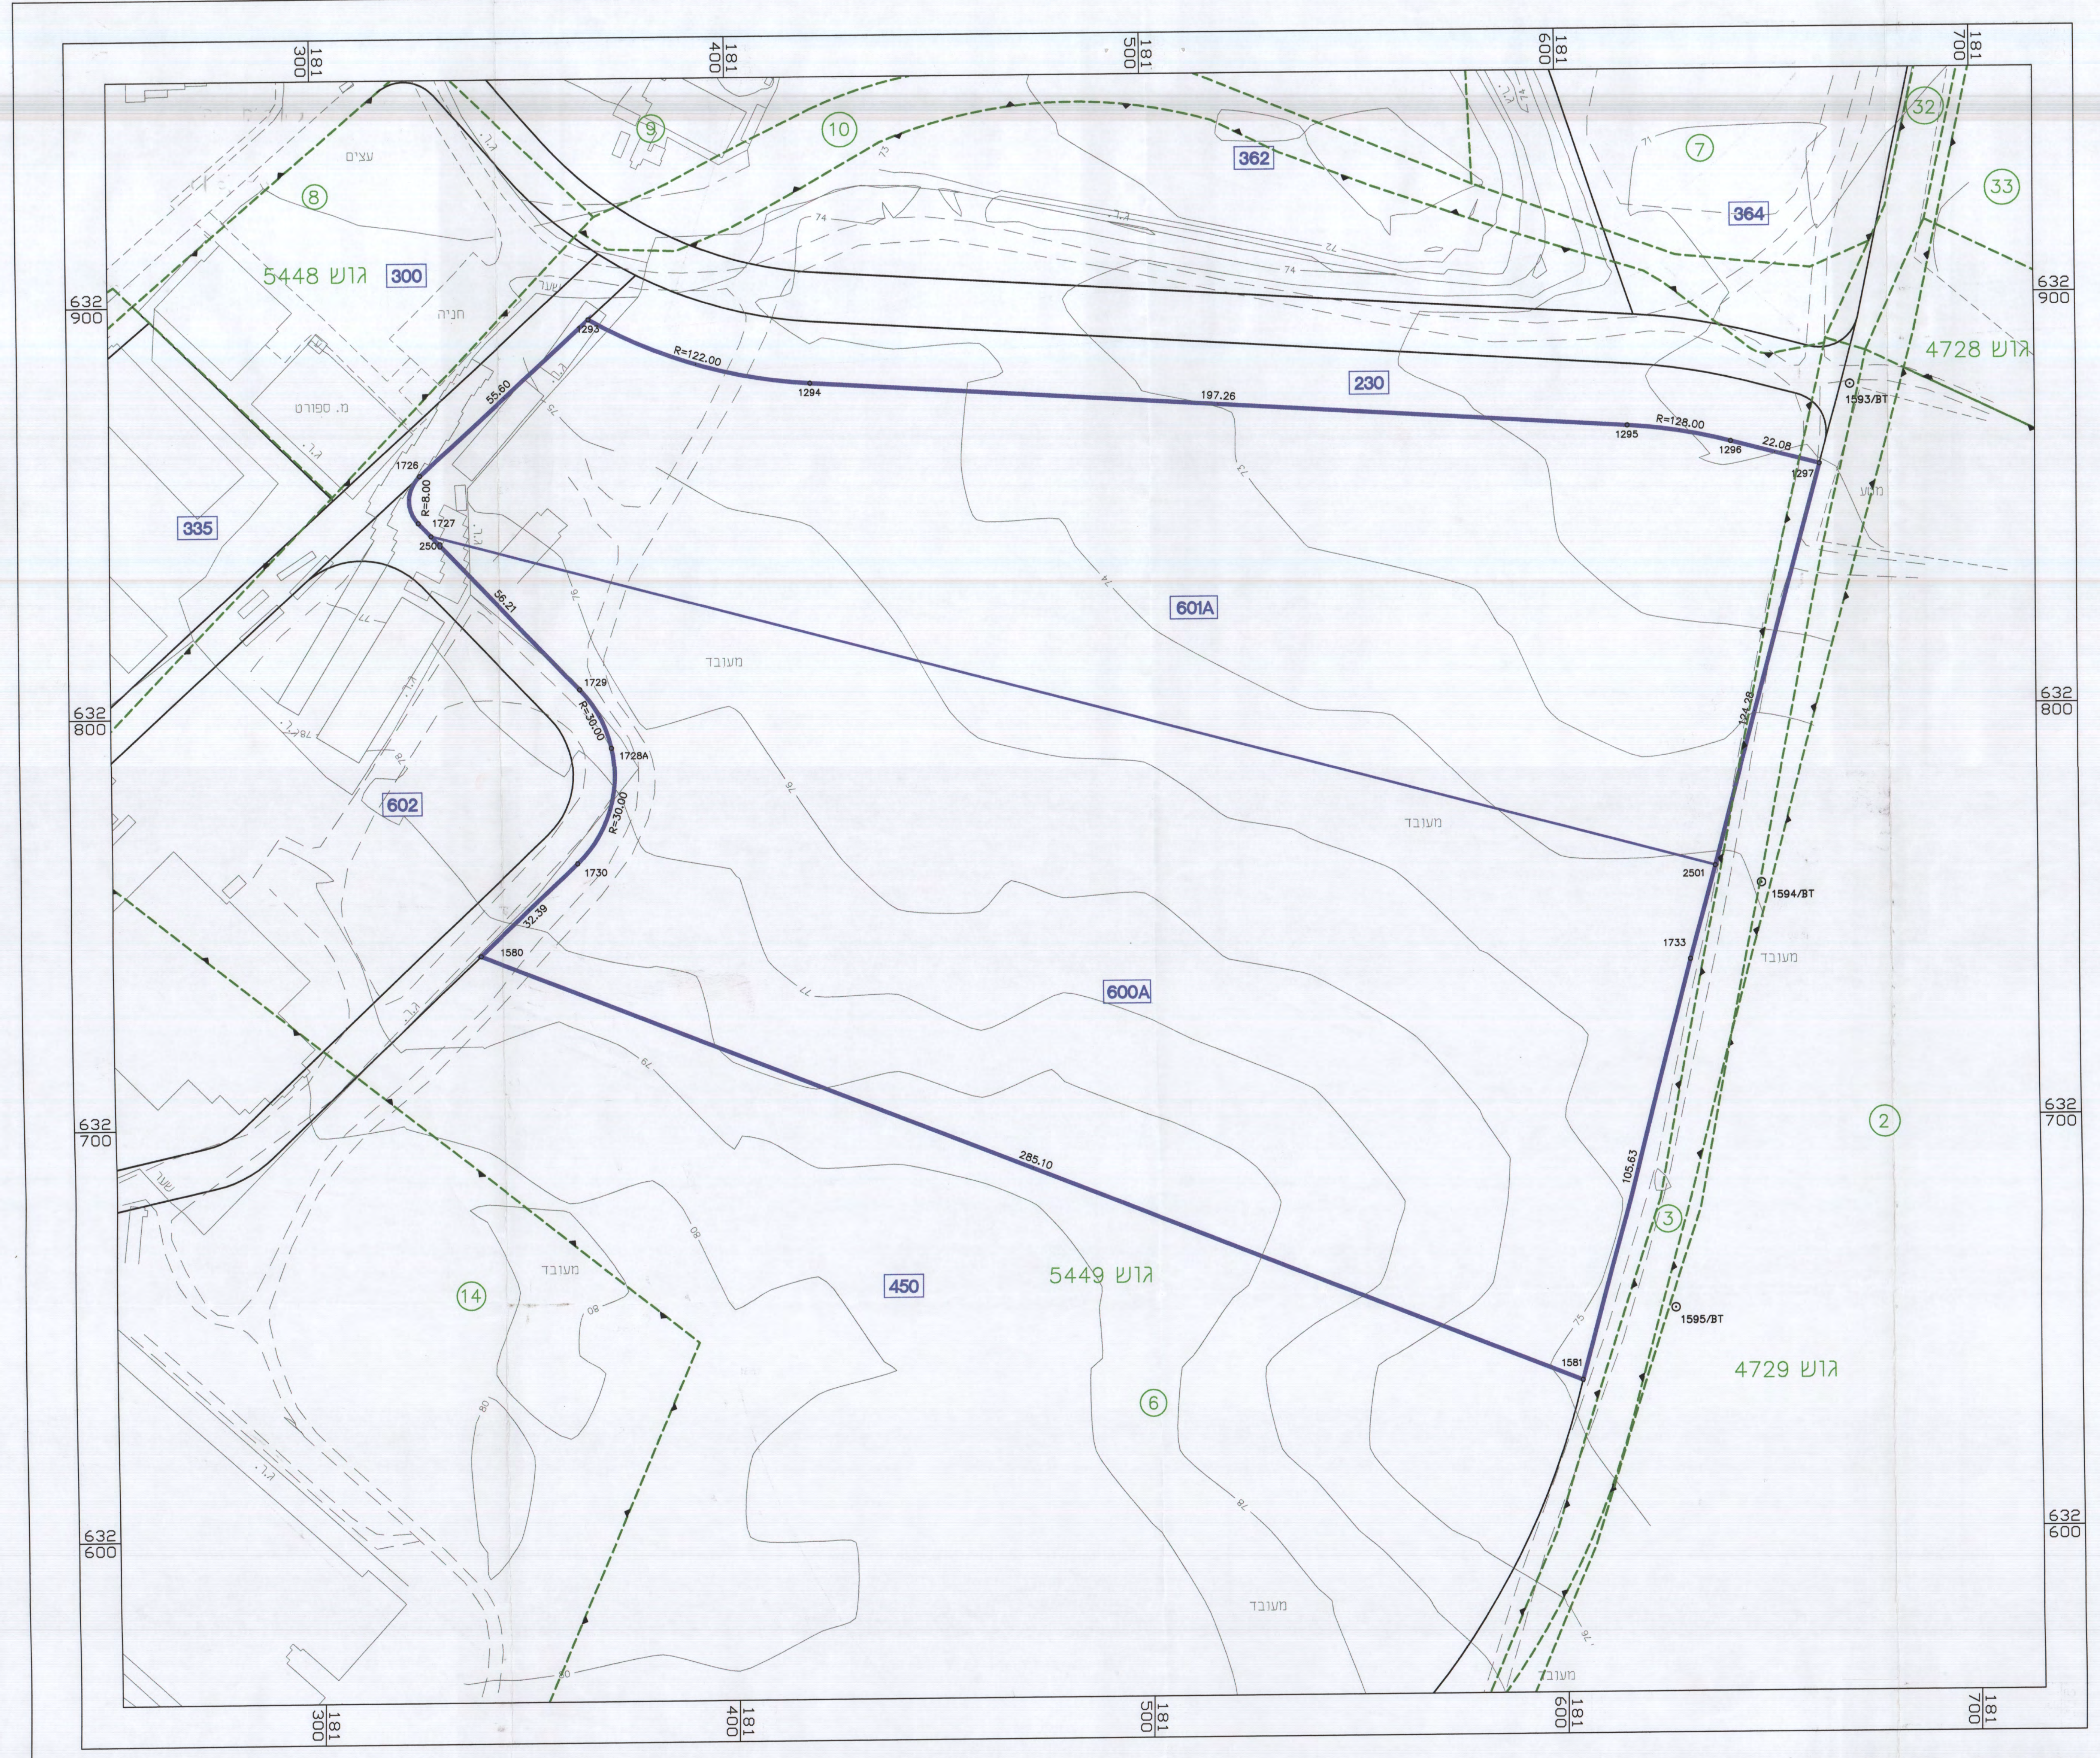

מצב מוצע קנ"מ 1 : 1000